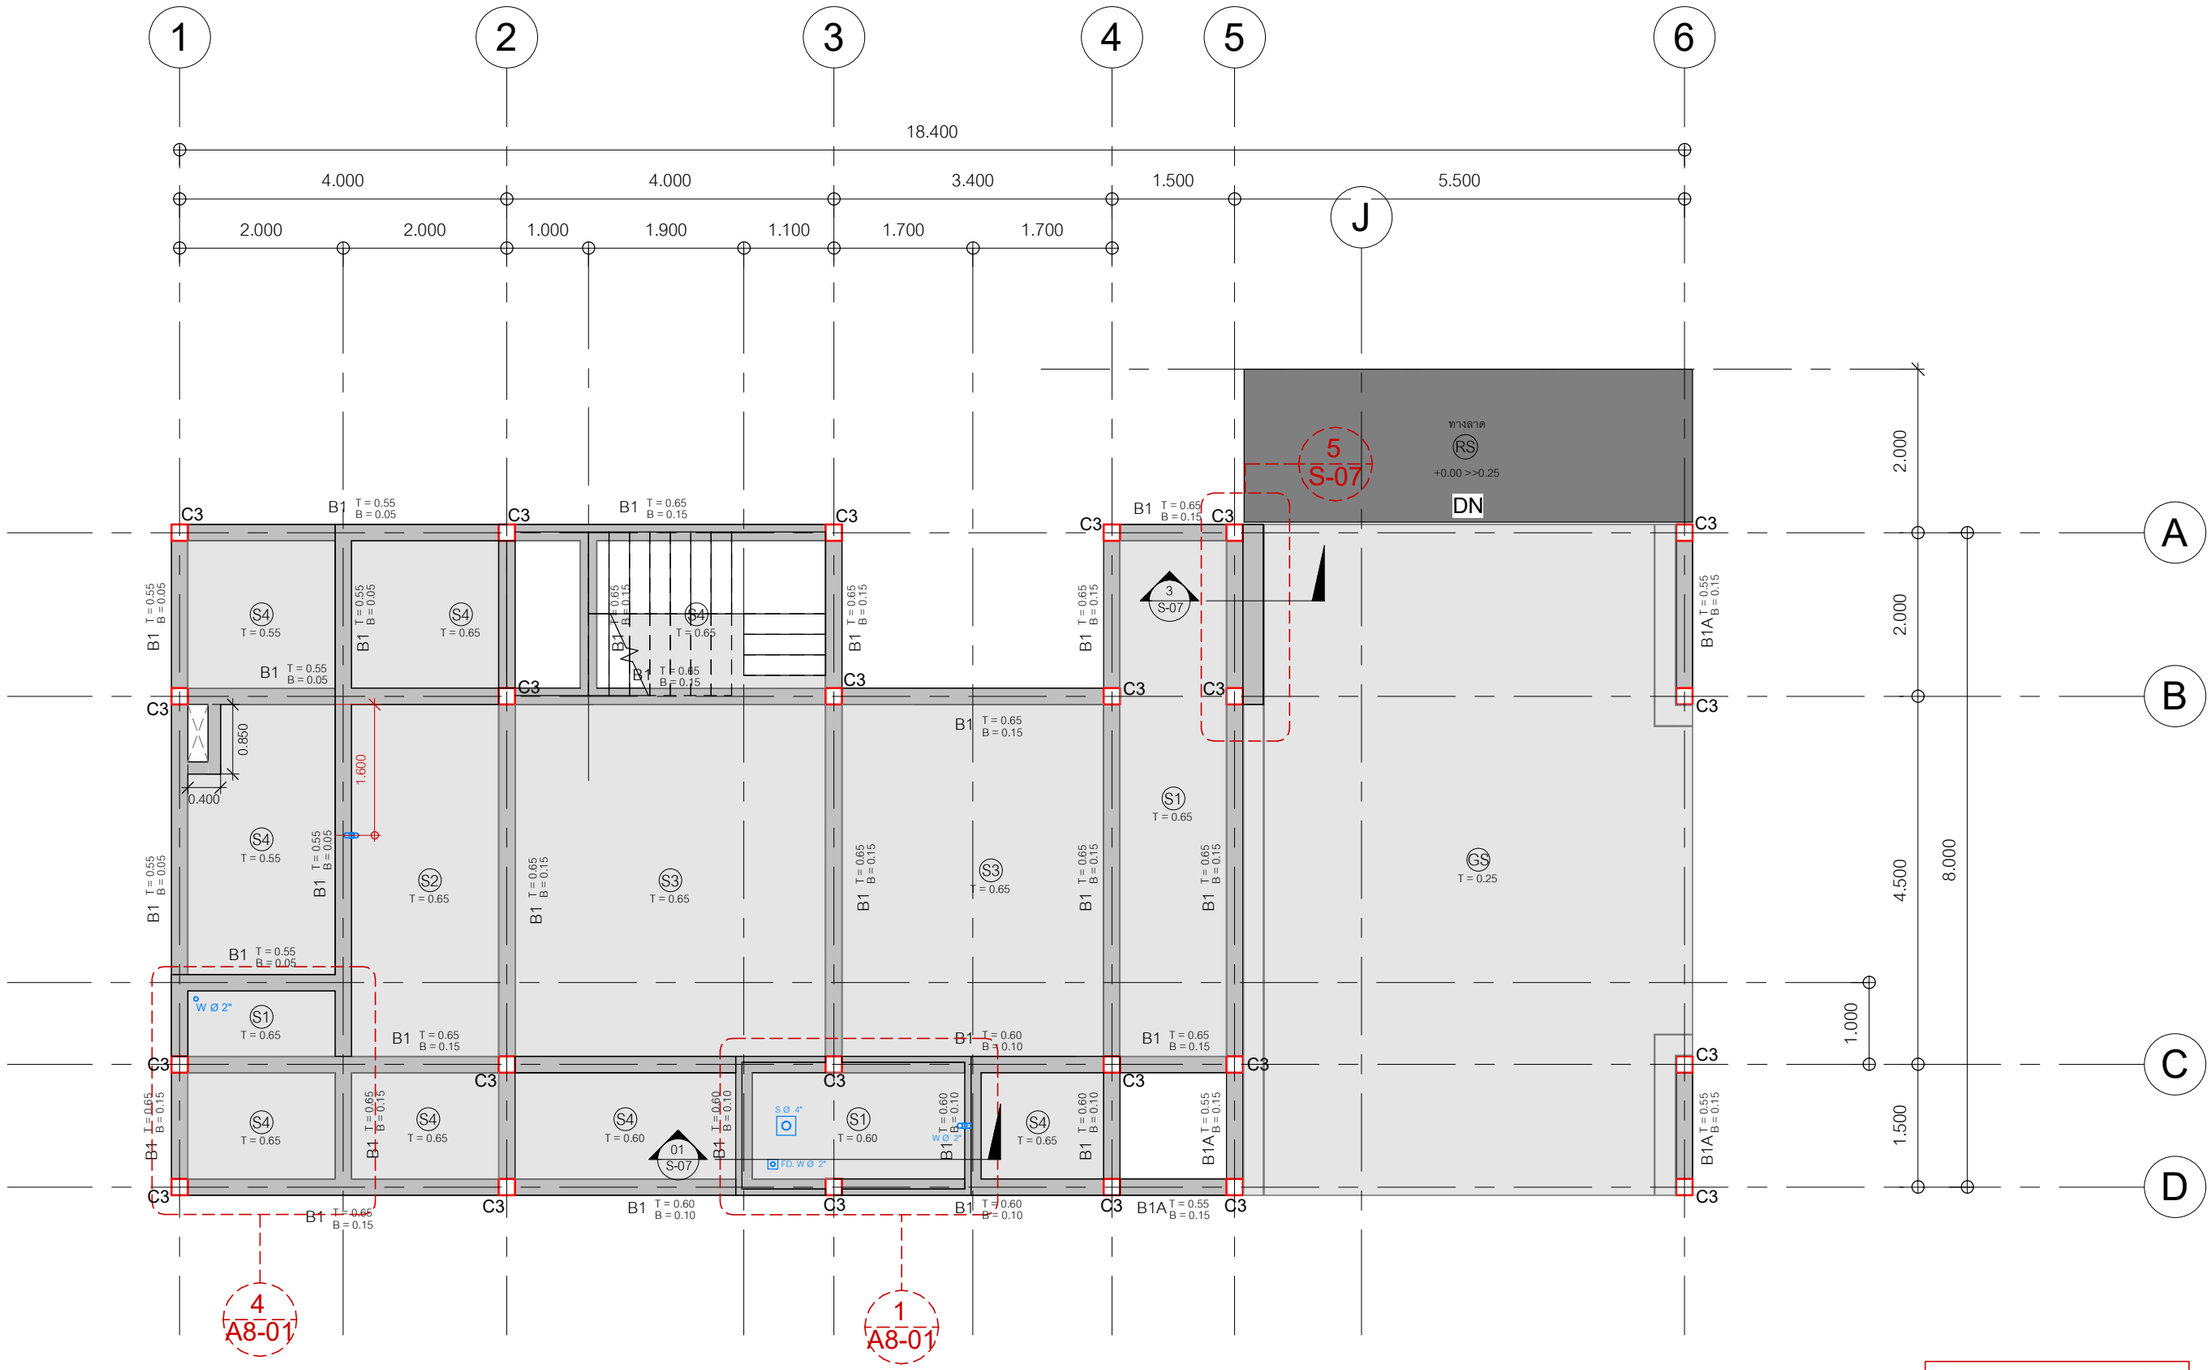


ความยาวแผ่นพื้น
2.55
PS
T = 0.45
ระดับ Top แผ่นพื้น
ไม่ใช่ระดับ Topping

หมายเหตุ : ระดับพื้นรอสรุปแบบ (ระดับพื้นมีการแก้ไข)

Siripantawi

บริการรับสร้างบ้าน
Tel : 092-862-3555 (คุณต่อ)
www.siripantawi.com

โครงการ (Project)

โครงการบ้านเดี่ยว 2 ชั้น

เจ้าของโครงการ (Owner)

คุณศุภกฤต เลิศคัมภีร์ศีล

สถานที่โครงการ (Project Site)

ซอยจอมทอง3 แขวงจอมทอง
เขตจอมทอง กทม. 10500

สถาปนิก (Architect)

คุณณัฐรียา ปรางจันทร์ ภ.-สถ. 27578

วิศวกรโครงสร้าง (Structural Engineer)

คุณธันทวัฒน์ ชันติชัยชจร ภย.74306

เขียนแบบ (Drawing)

คุณสุภัสสรา พงษ์พิศาล

ID : SPW-FORCON-261022-01

แบบแก้ไข (Revision)

NO.	DATE	DESCRIPTION

แบบแสดง (Drawing Title)

แปลนคานชั้น 1

มาตราส่วน (SCALE)	1 : 75
(Paper)	(Drawing No)
A3	S-03

แบบที่แสดงในแผ่นที่ เป็นทรัพย์สินของ
บริษัท สิริบันทวี จำกัด
ห้ามทำซ้ำ คัดลอก หรือ จำลองโดยมิได้รับ
อนุญาตจาก บริษัท สิริบันทวี จำกัด